
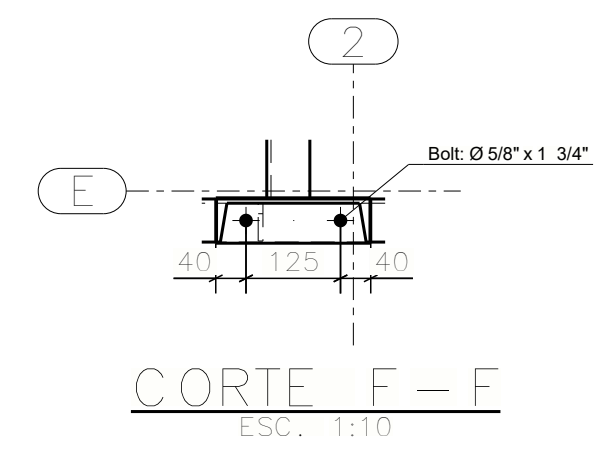
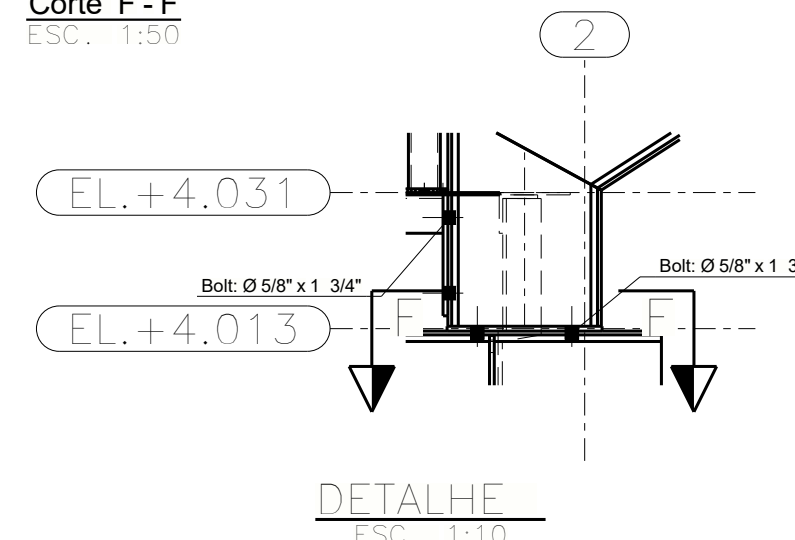
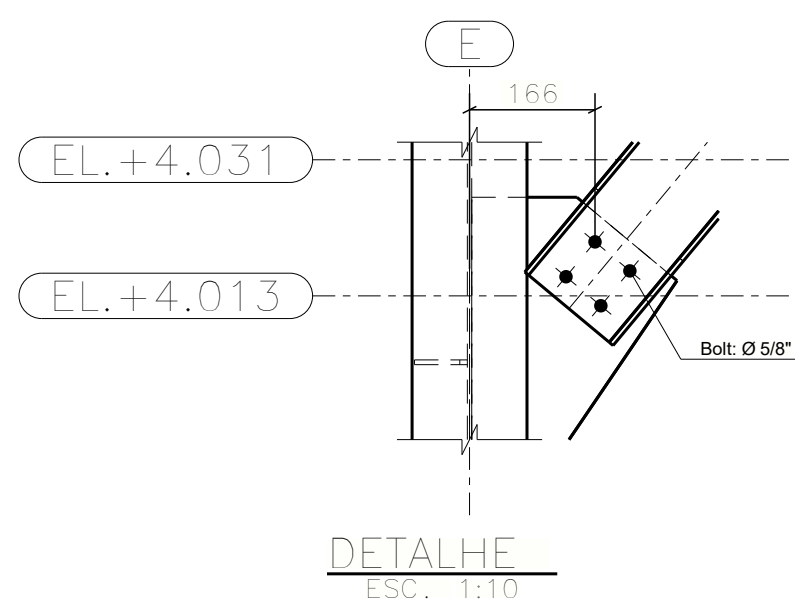
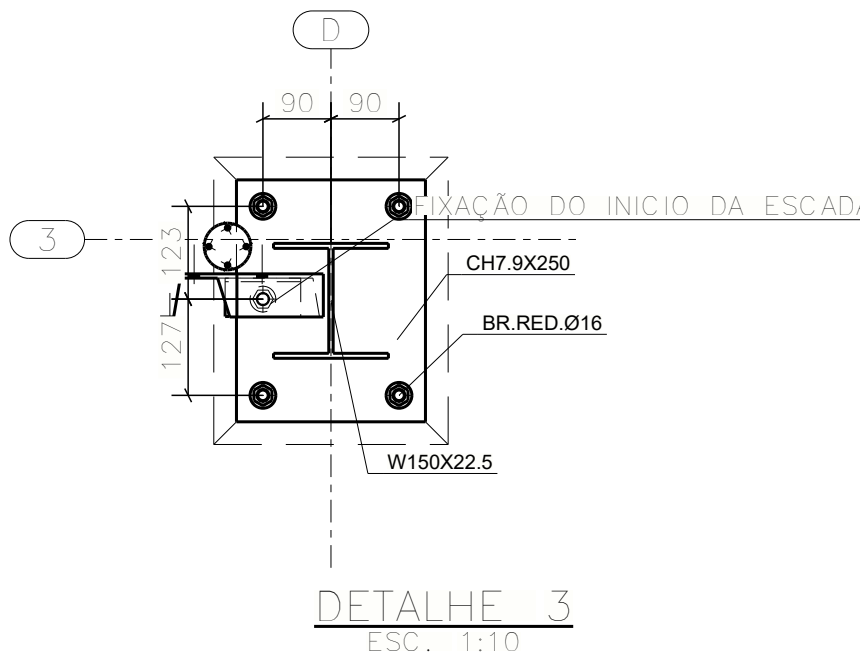
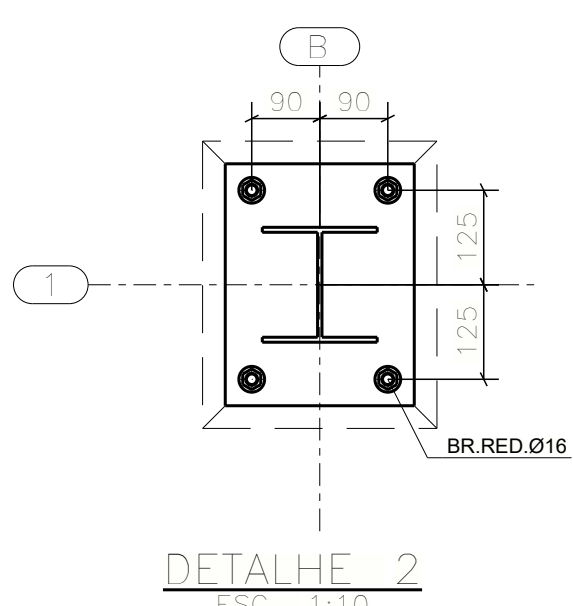
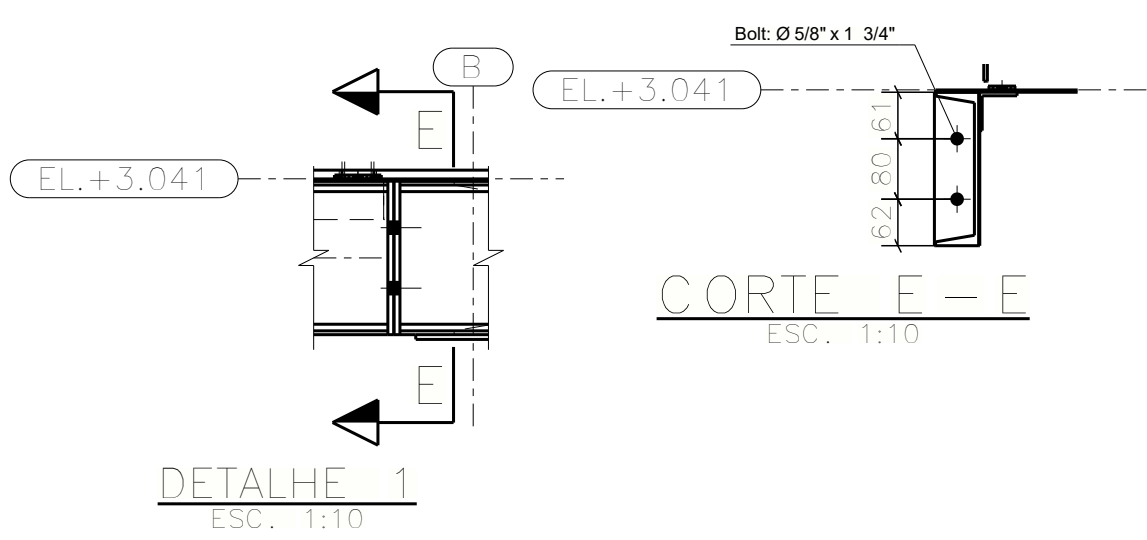
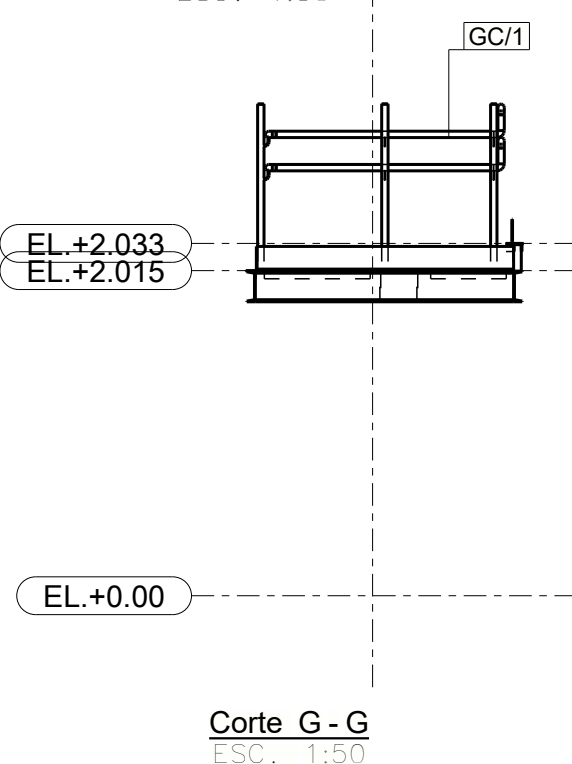
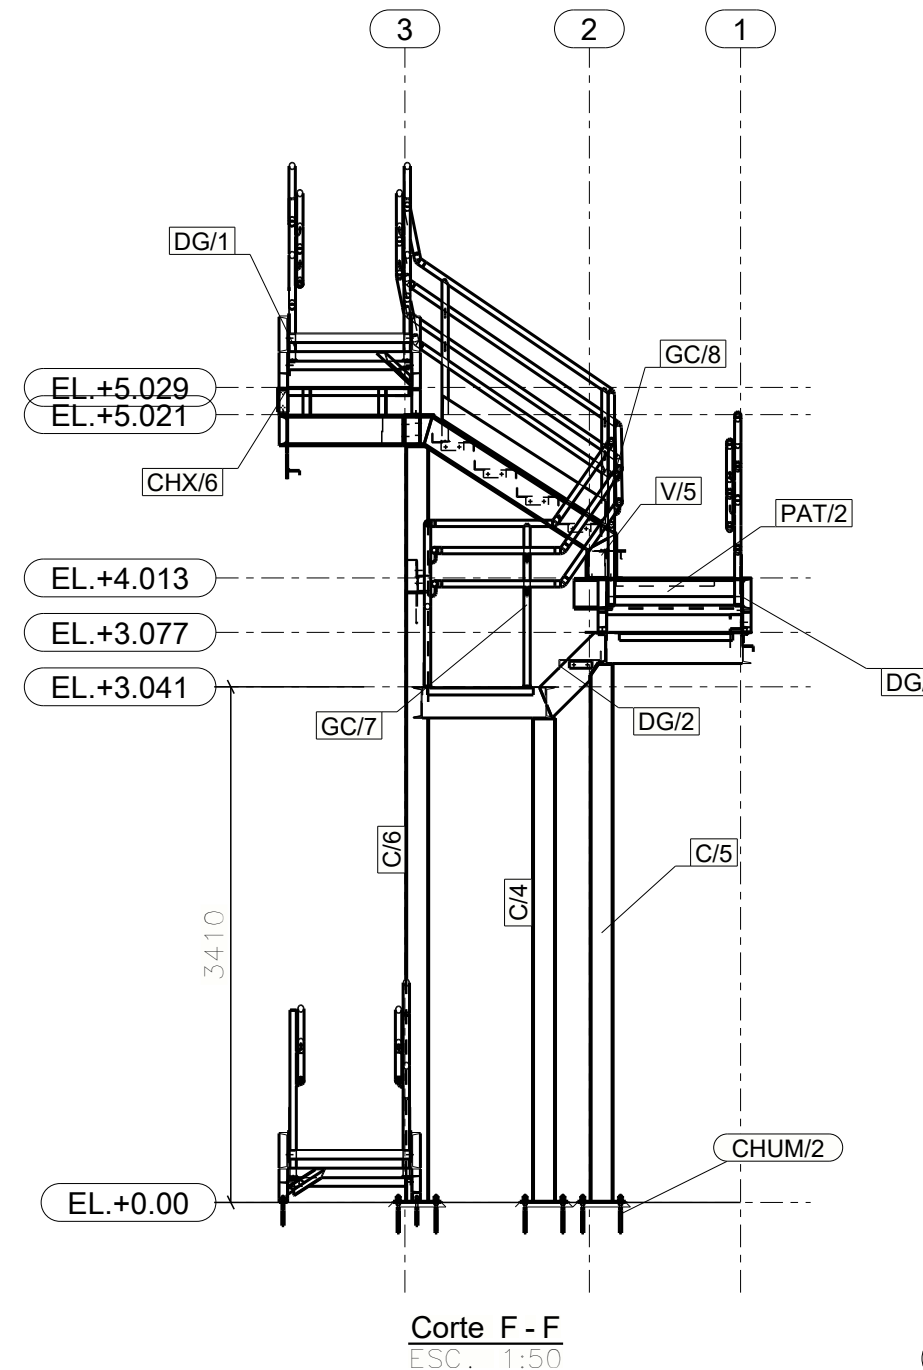
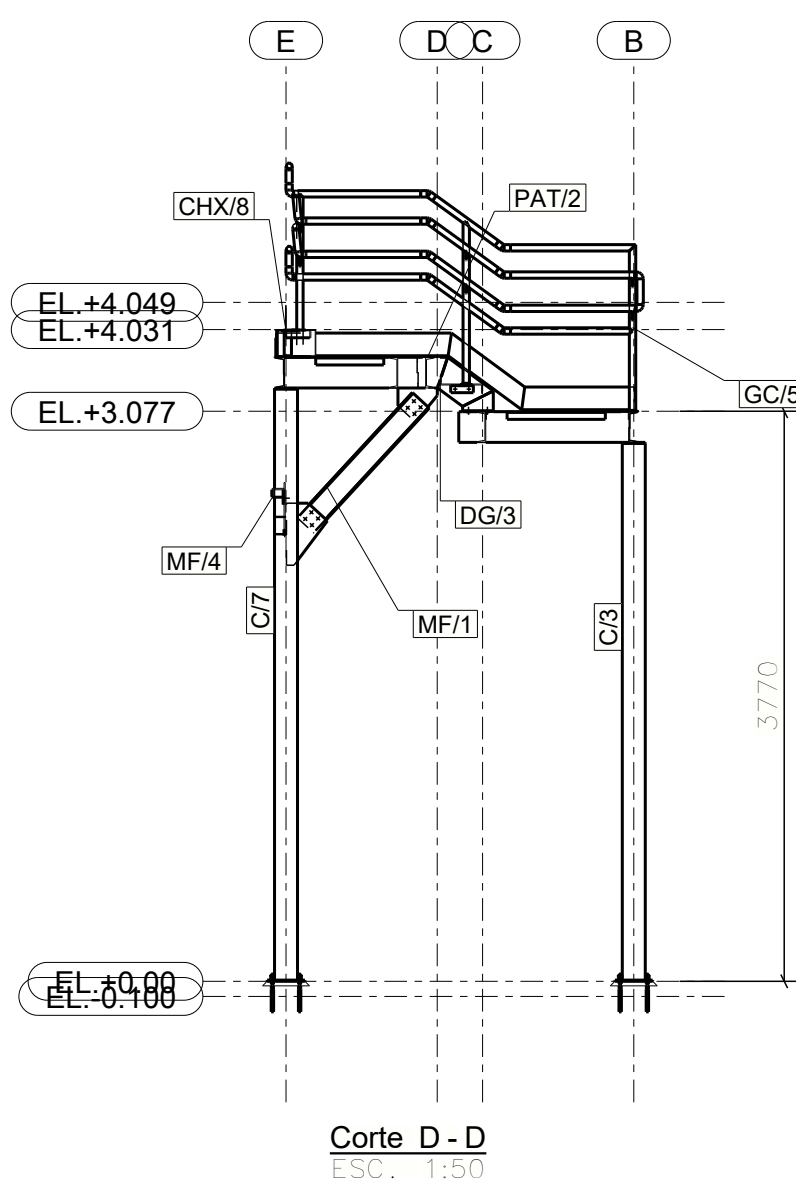
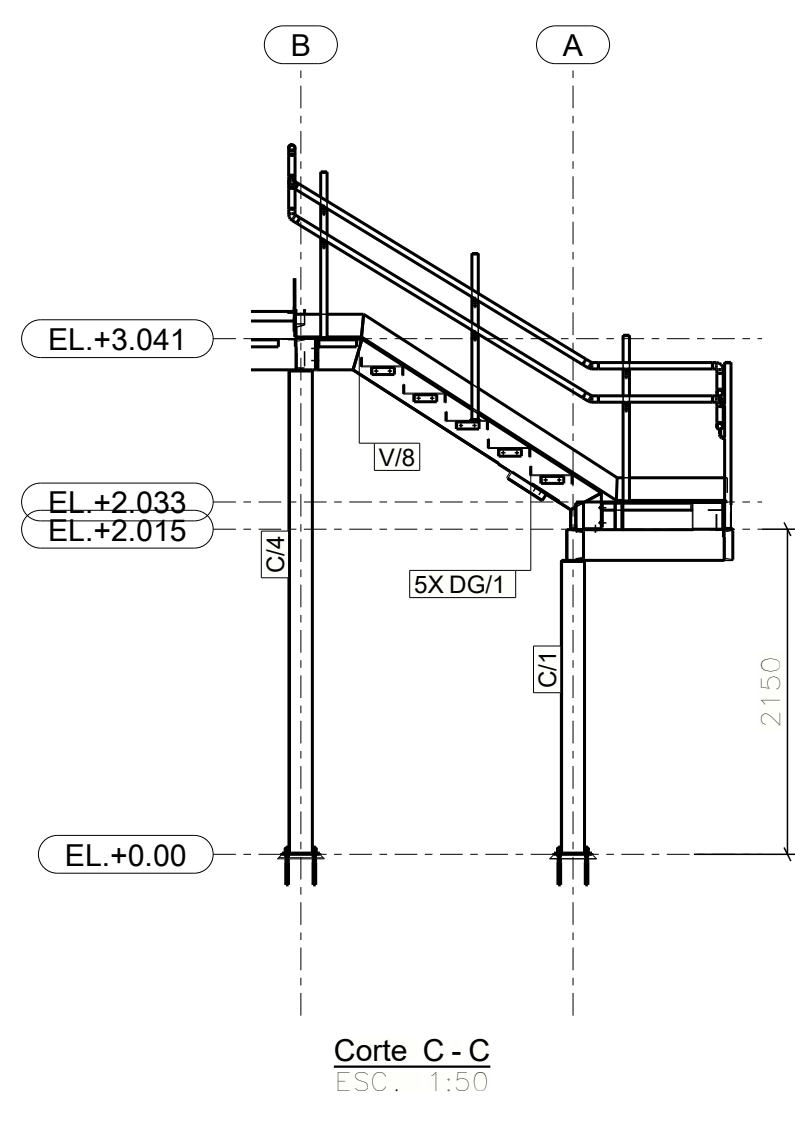
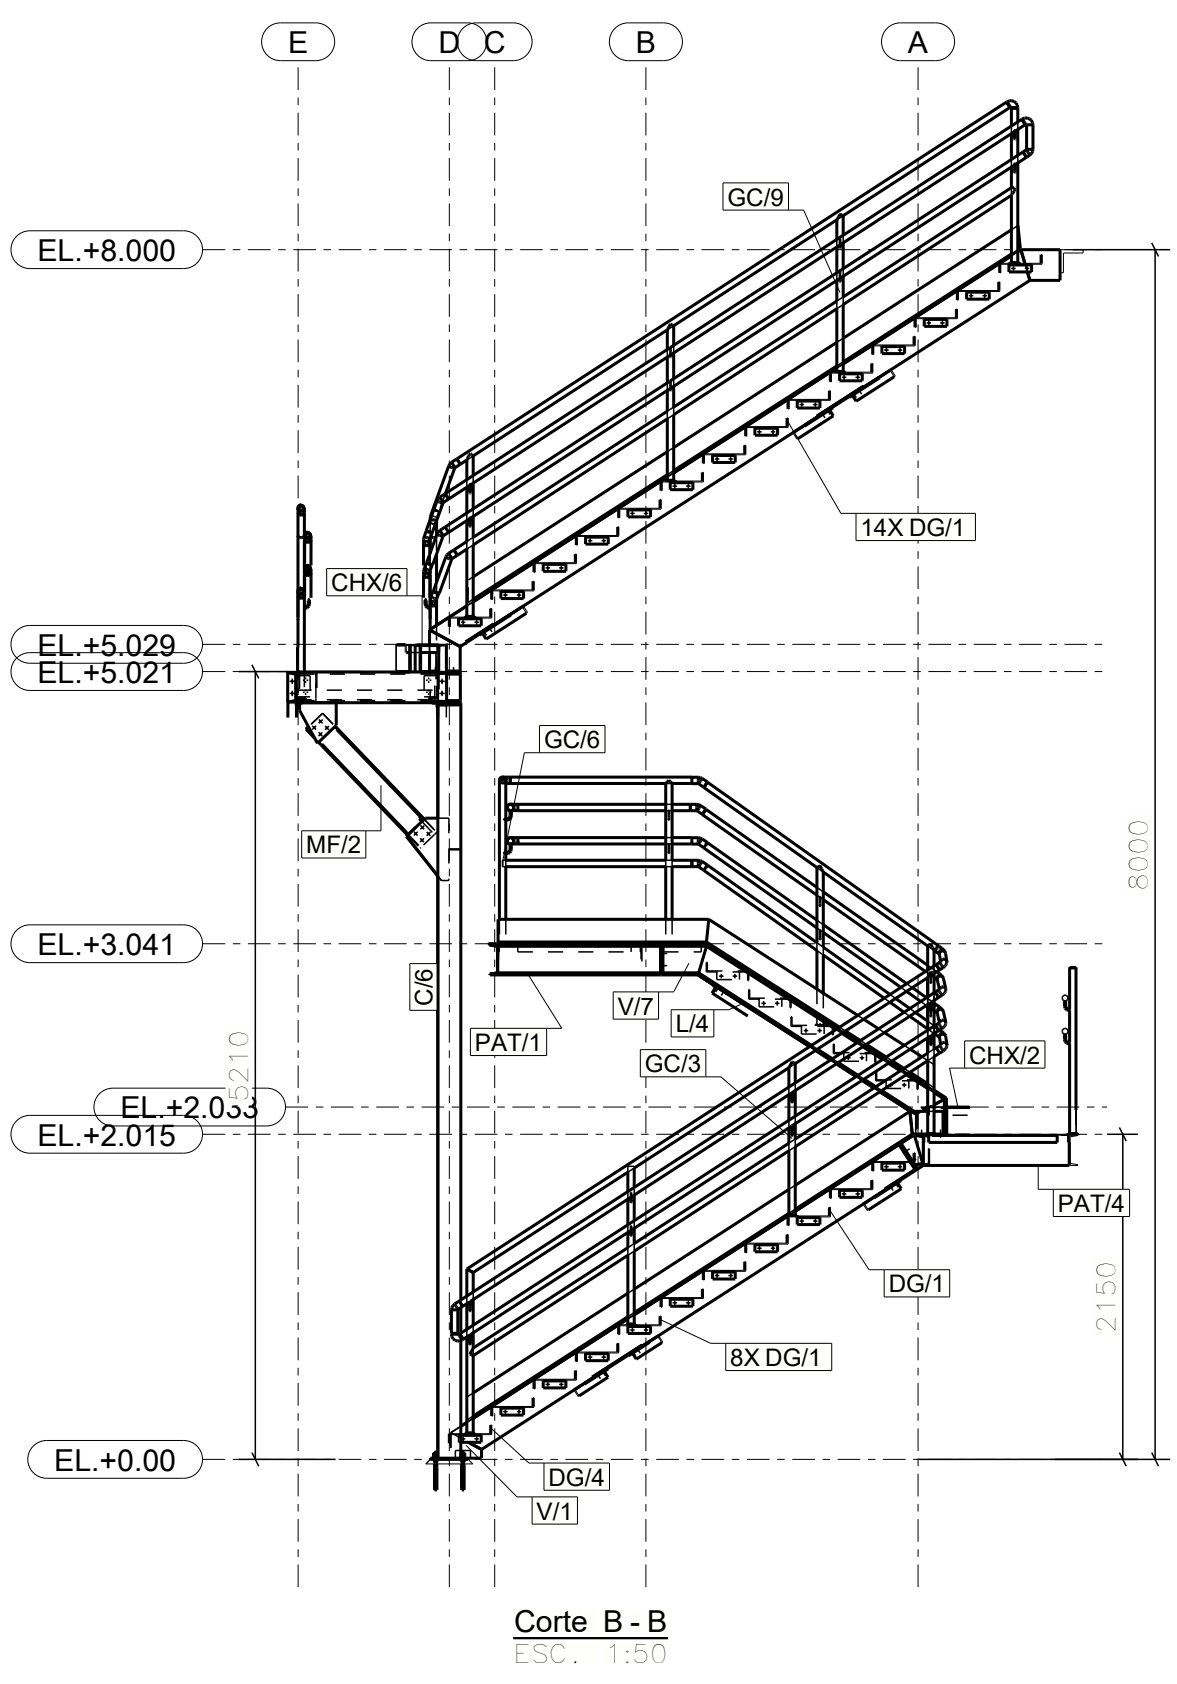
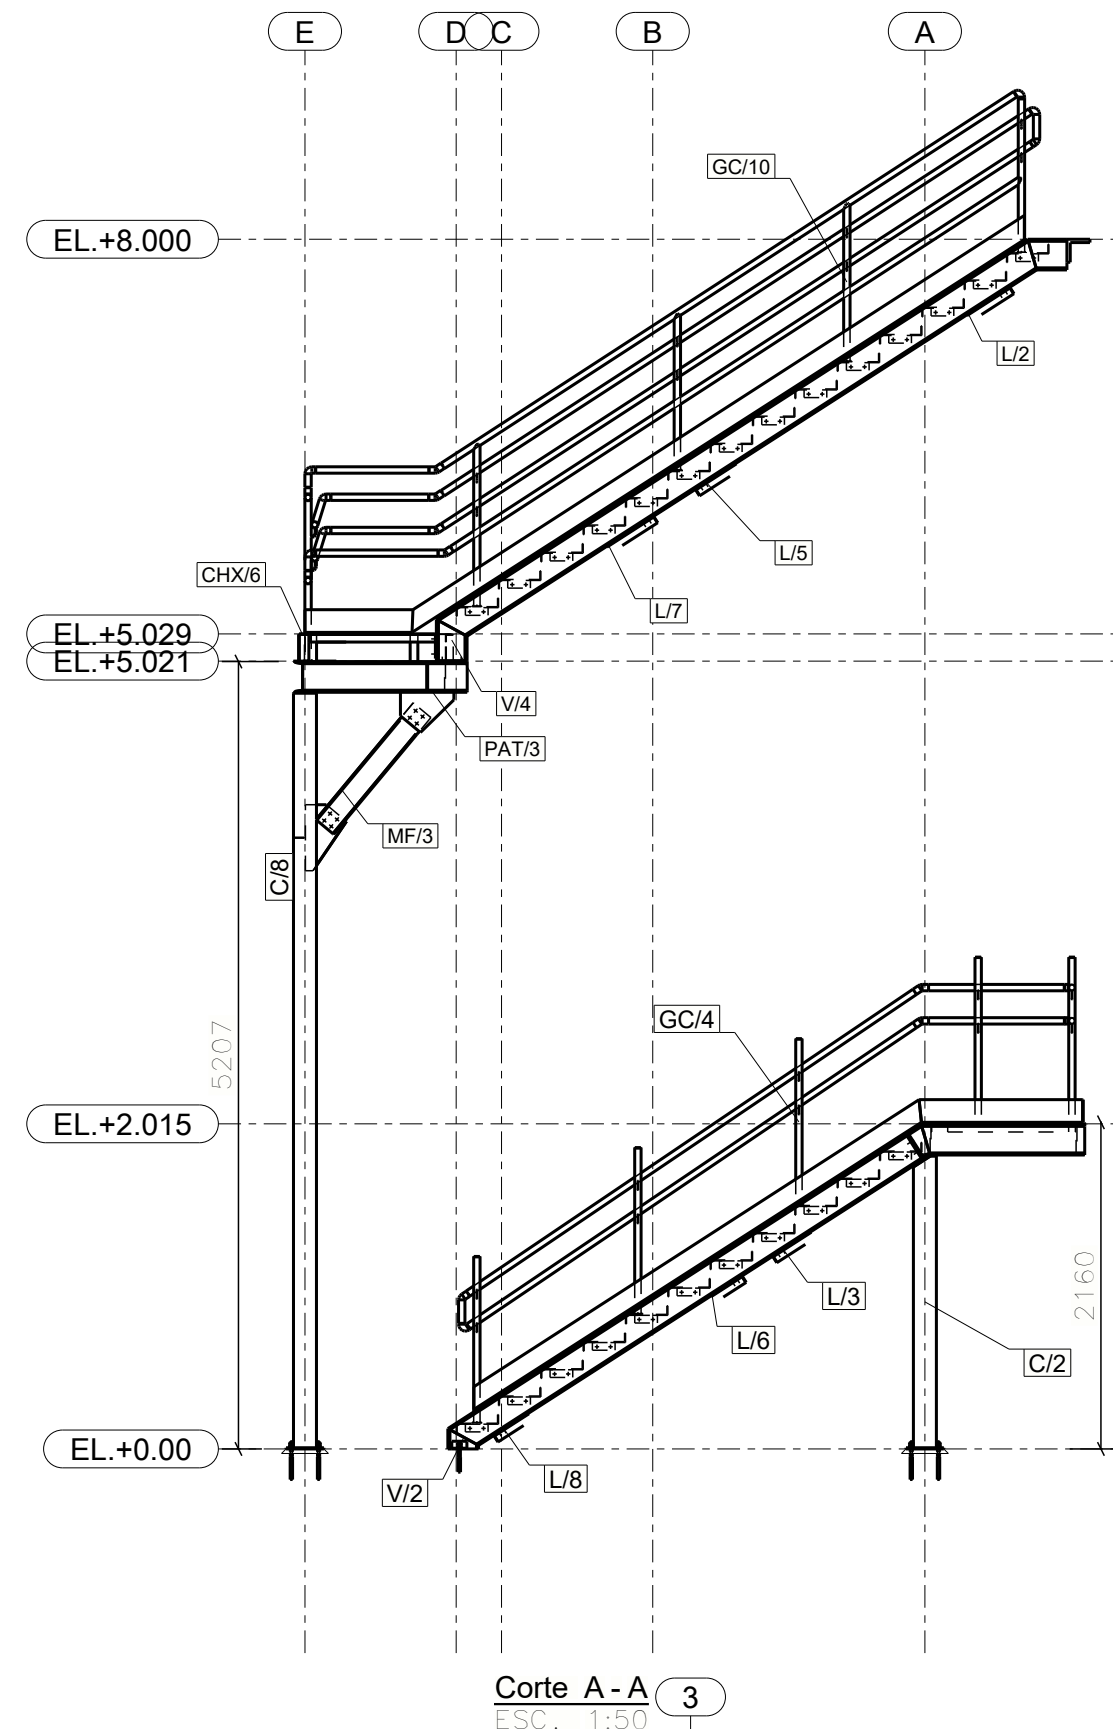
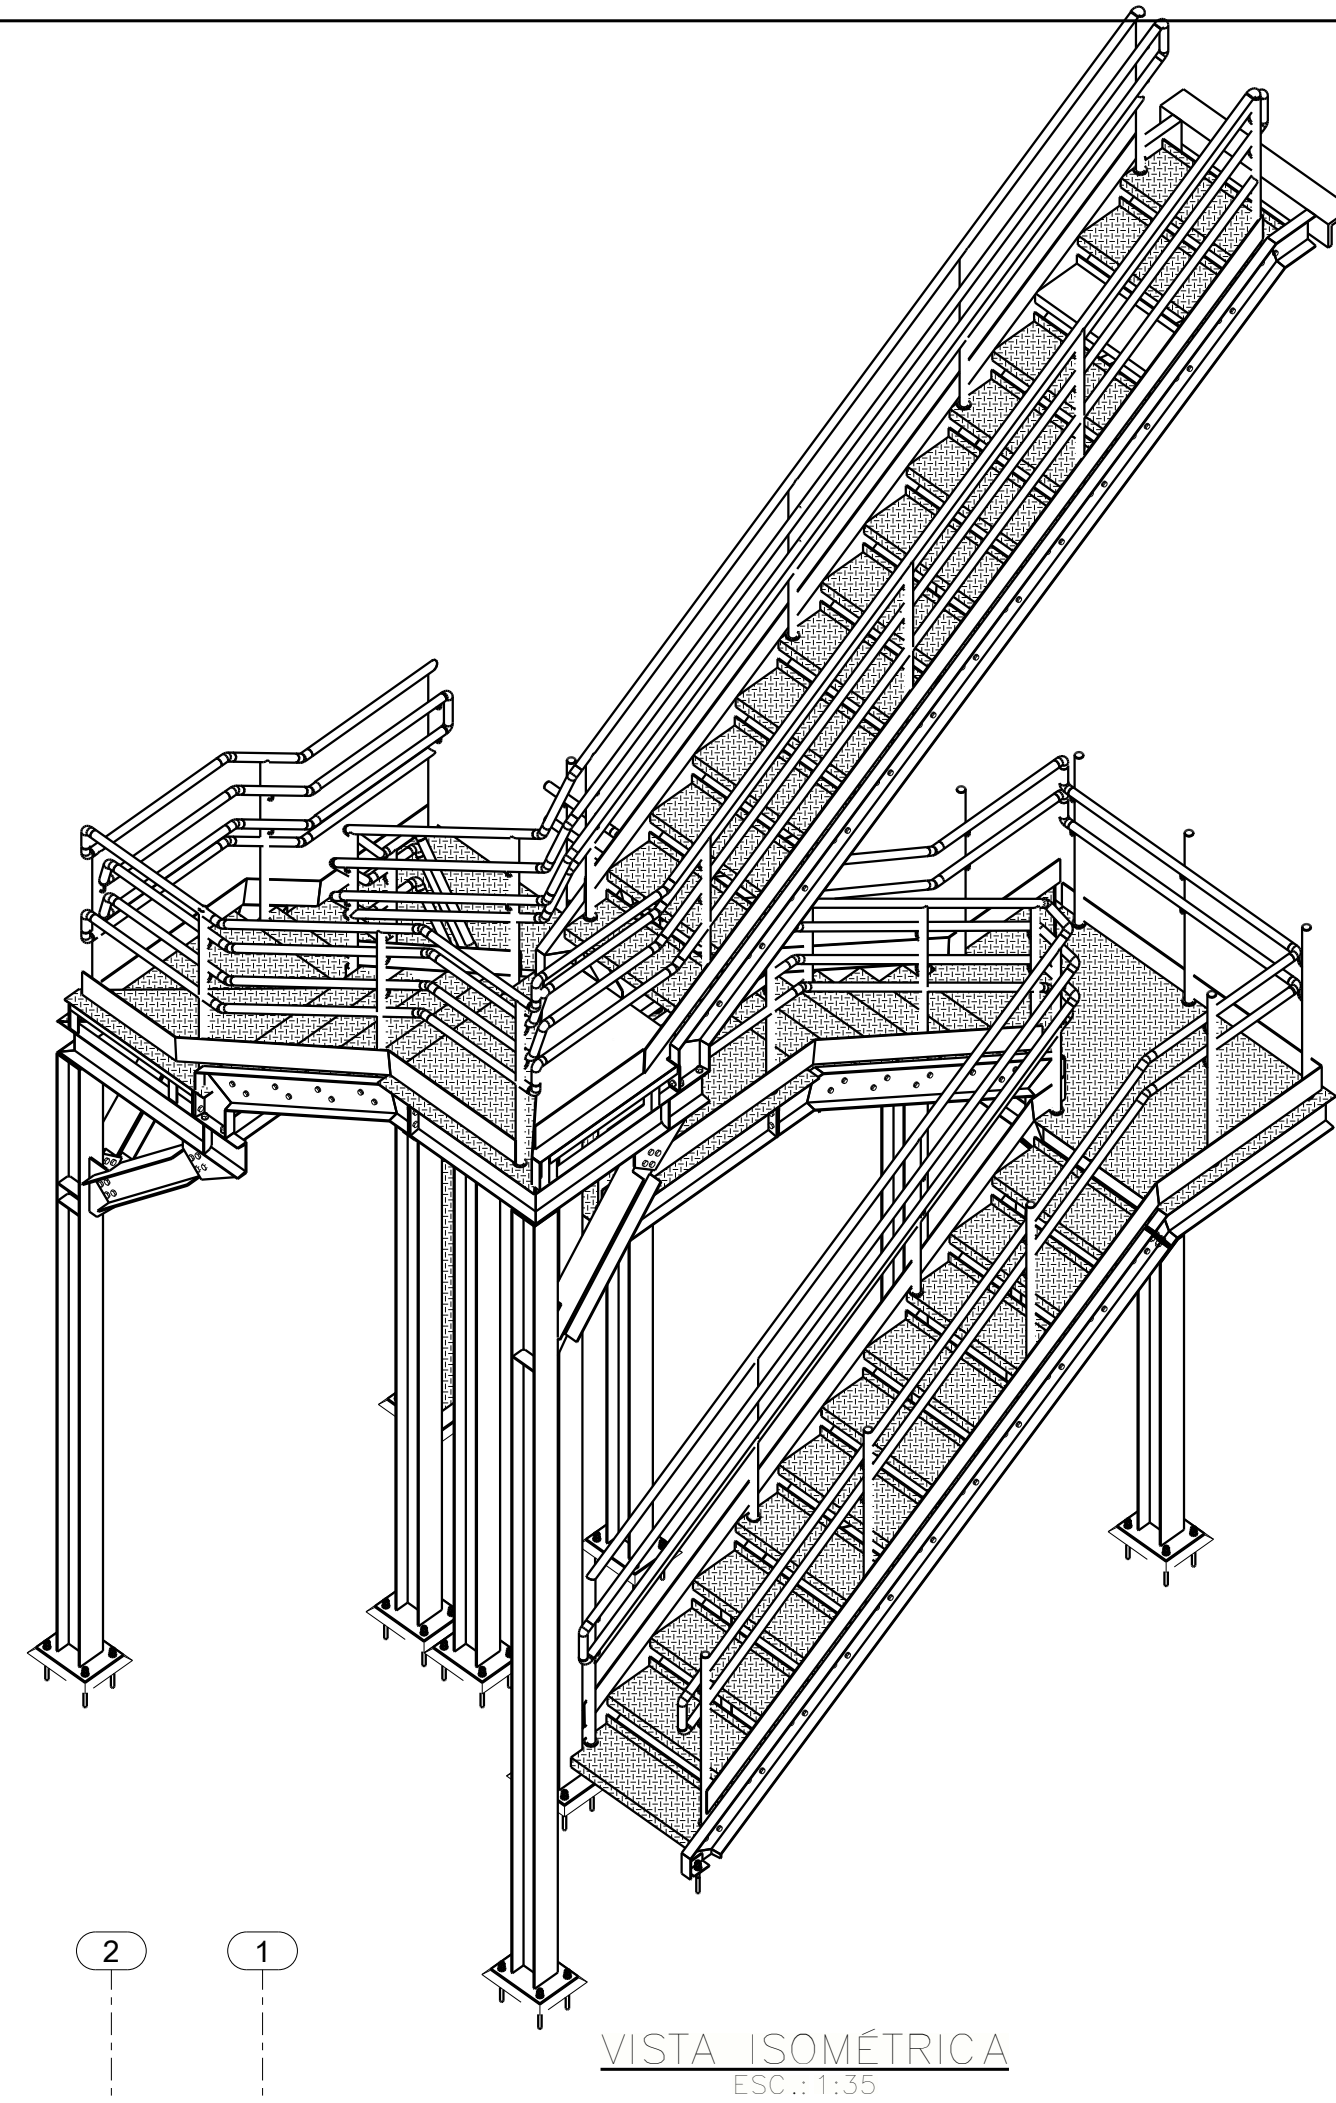
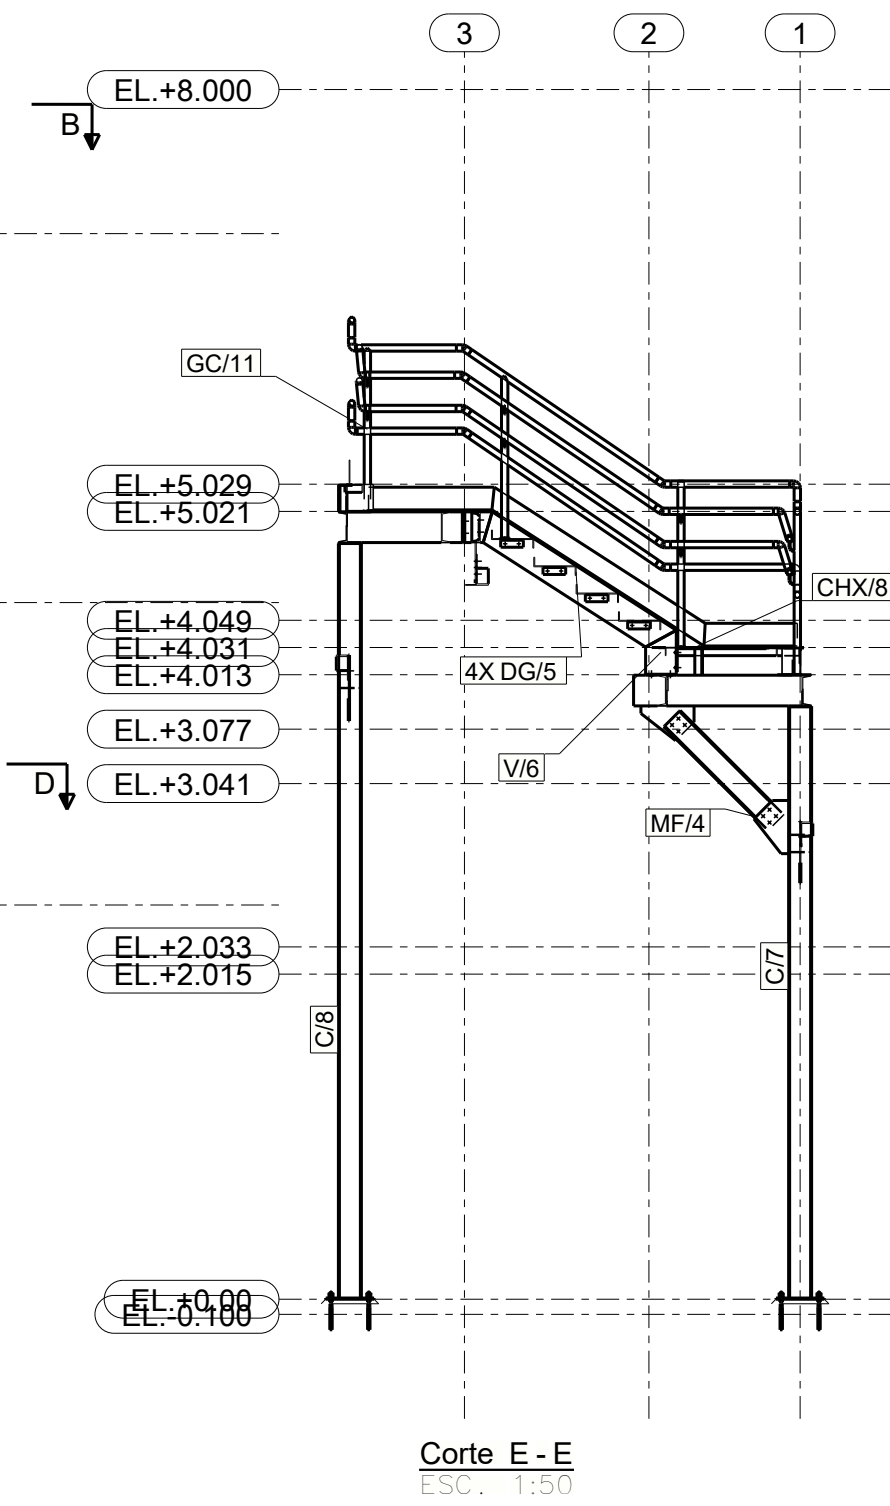
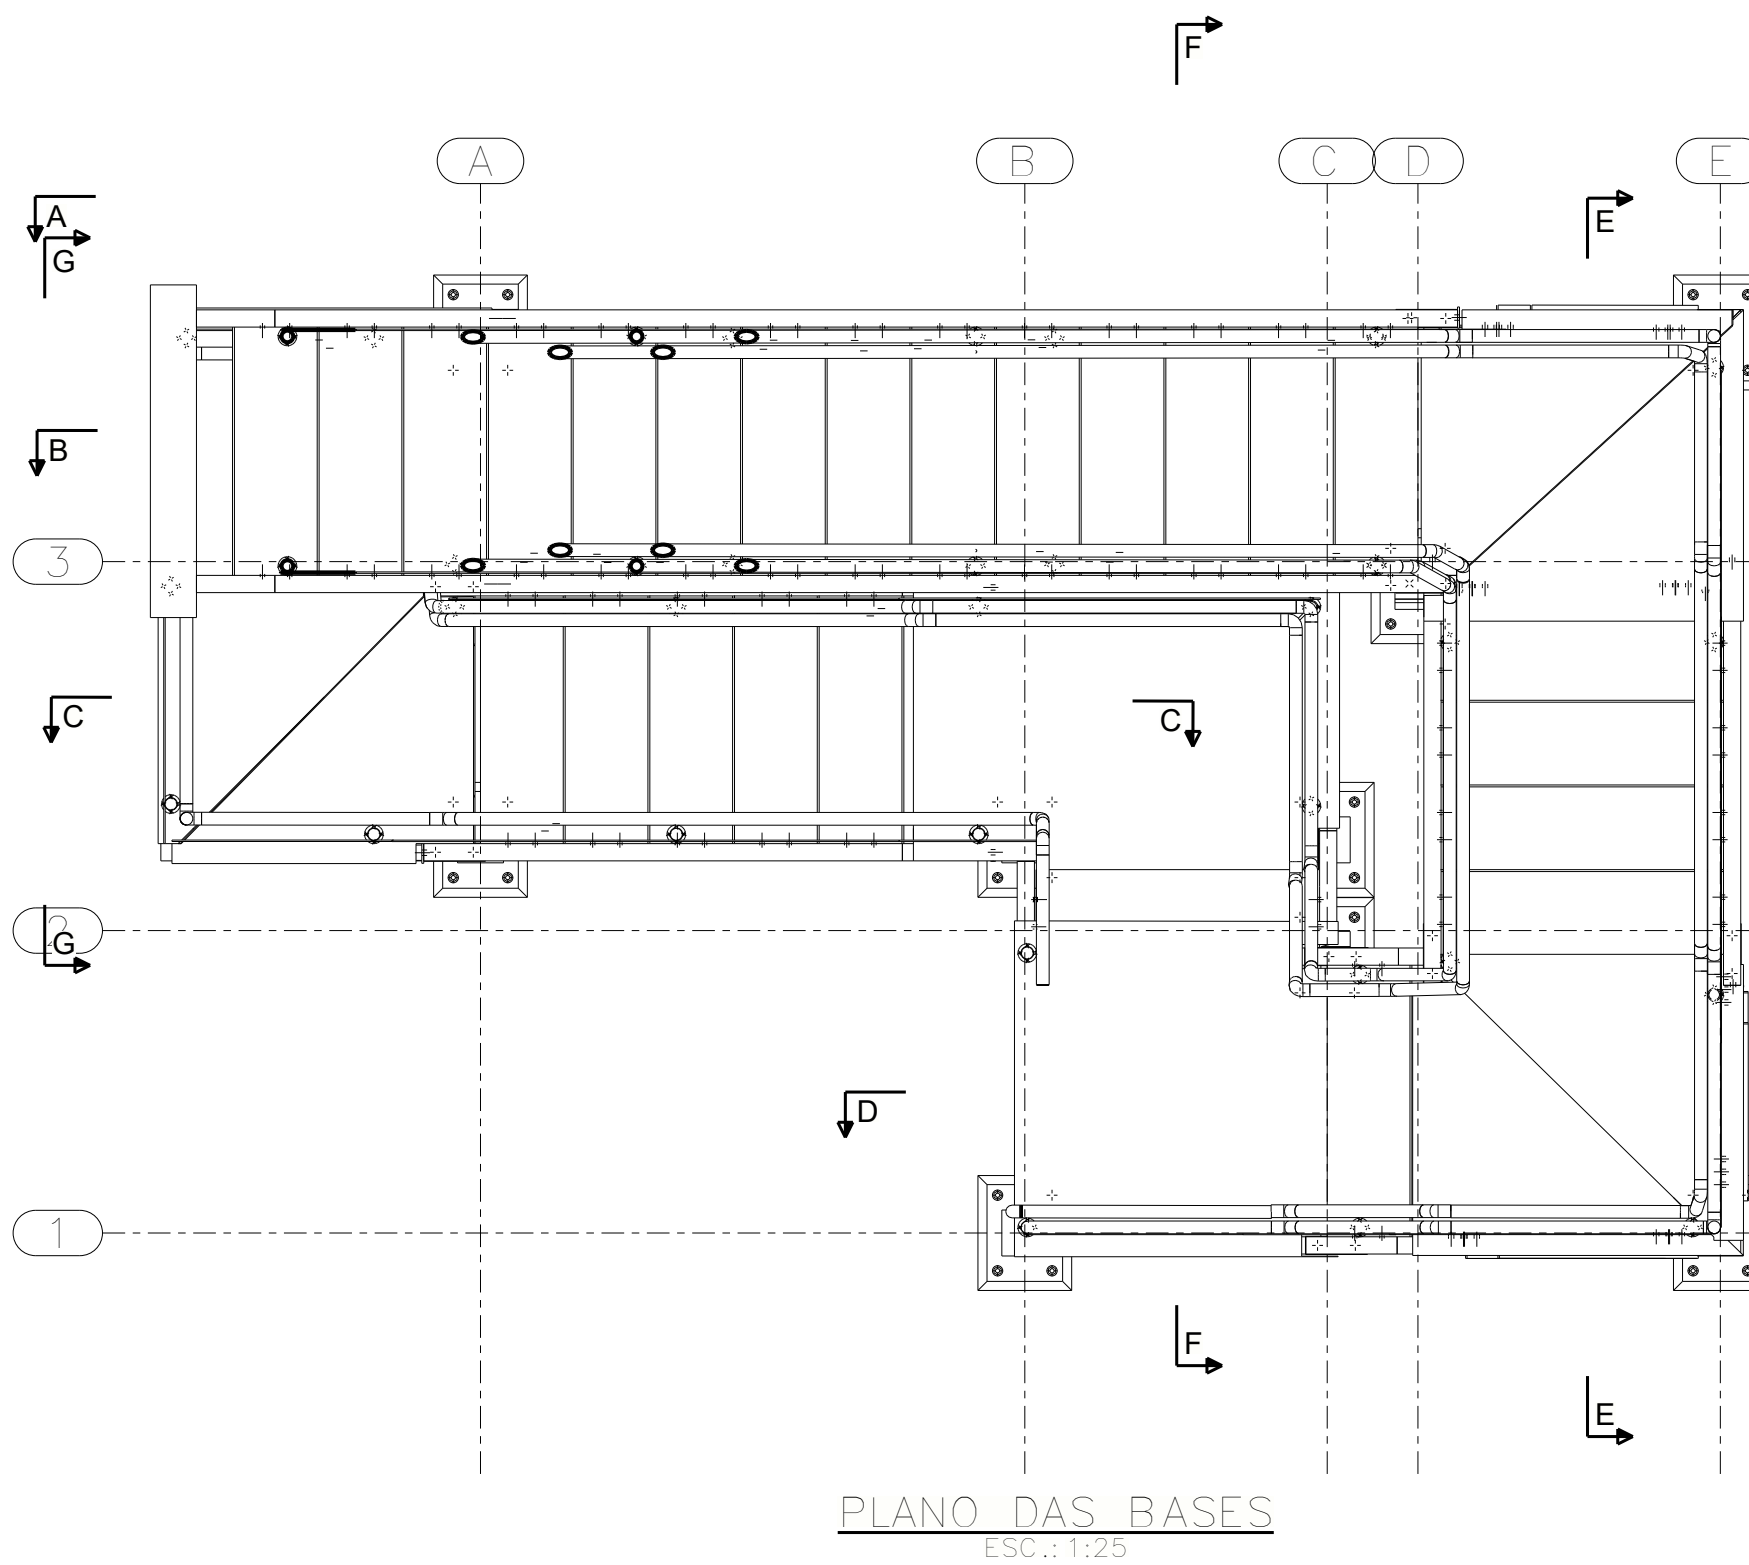


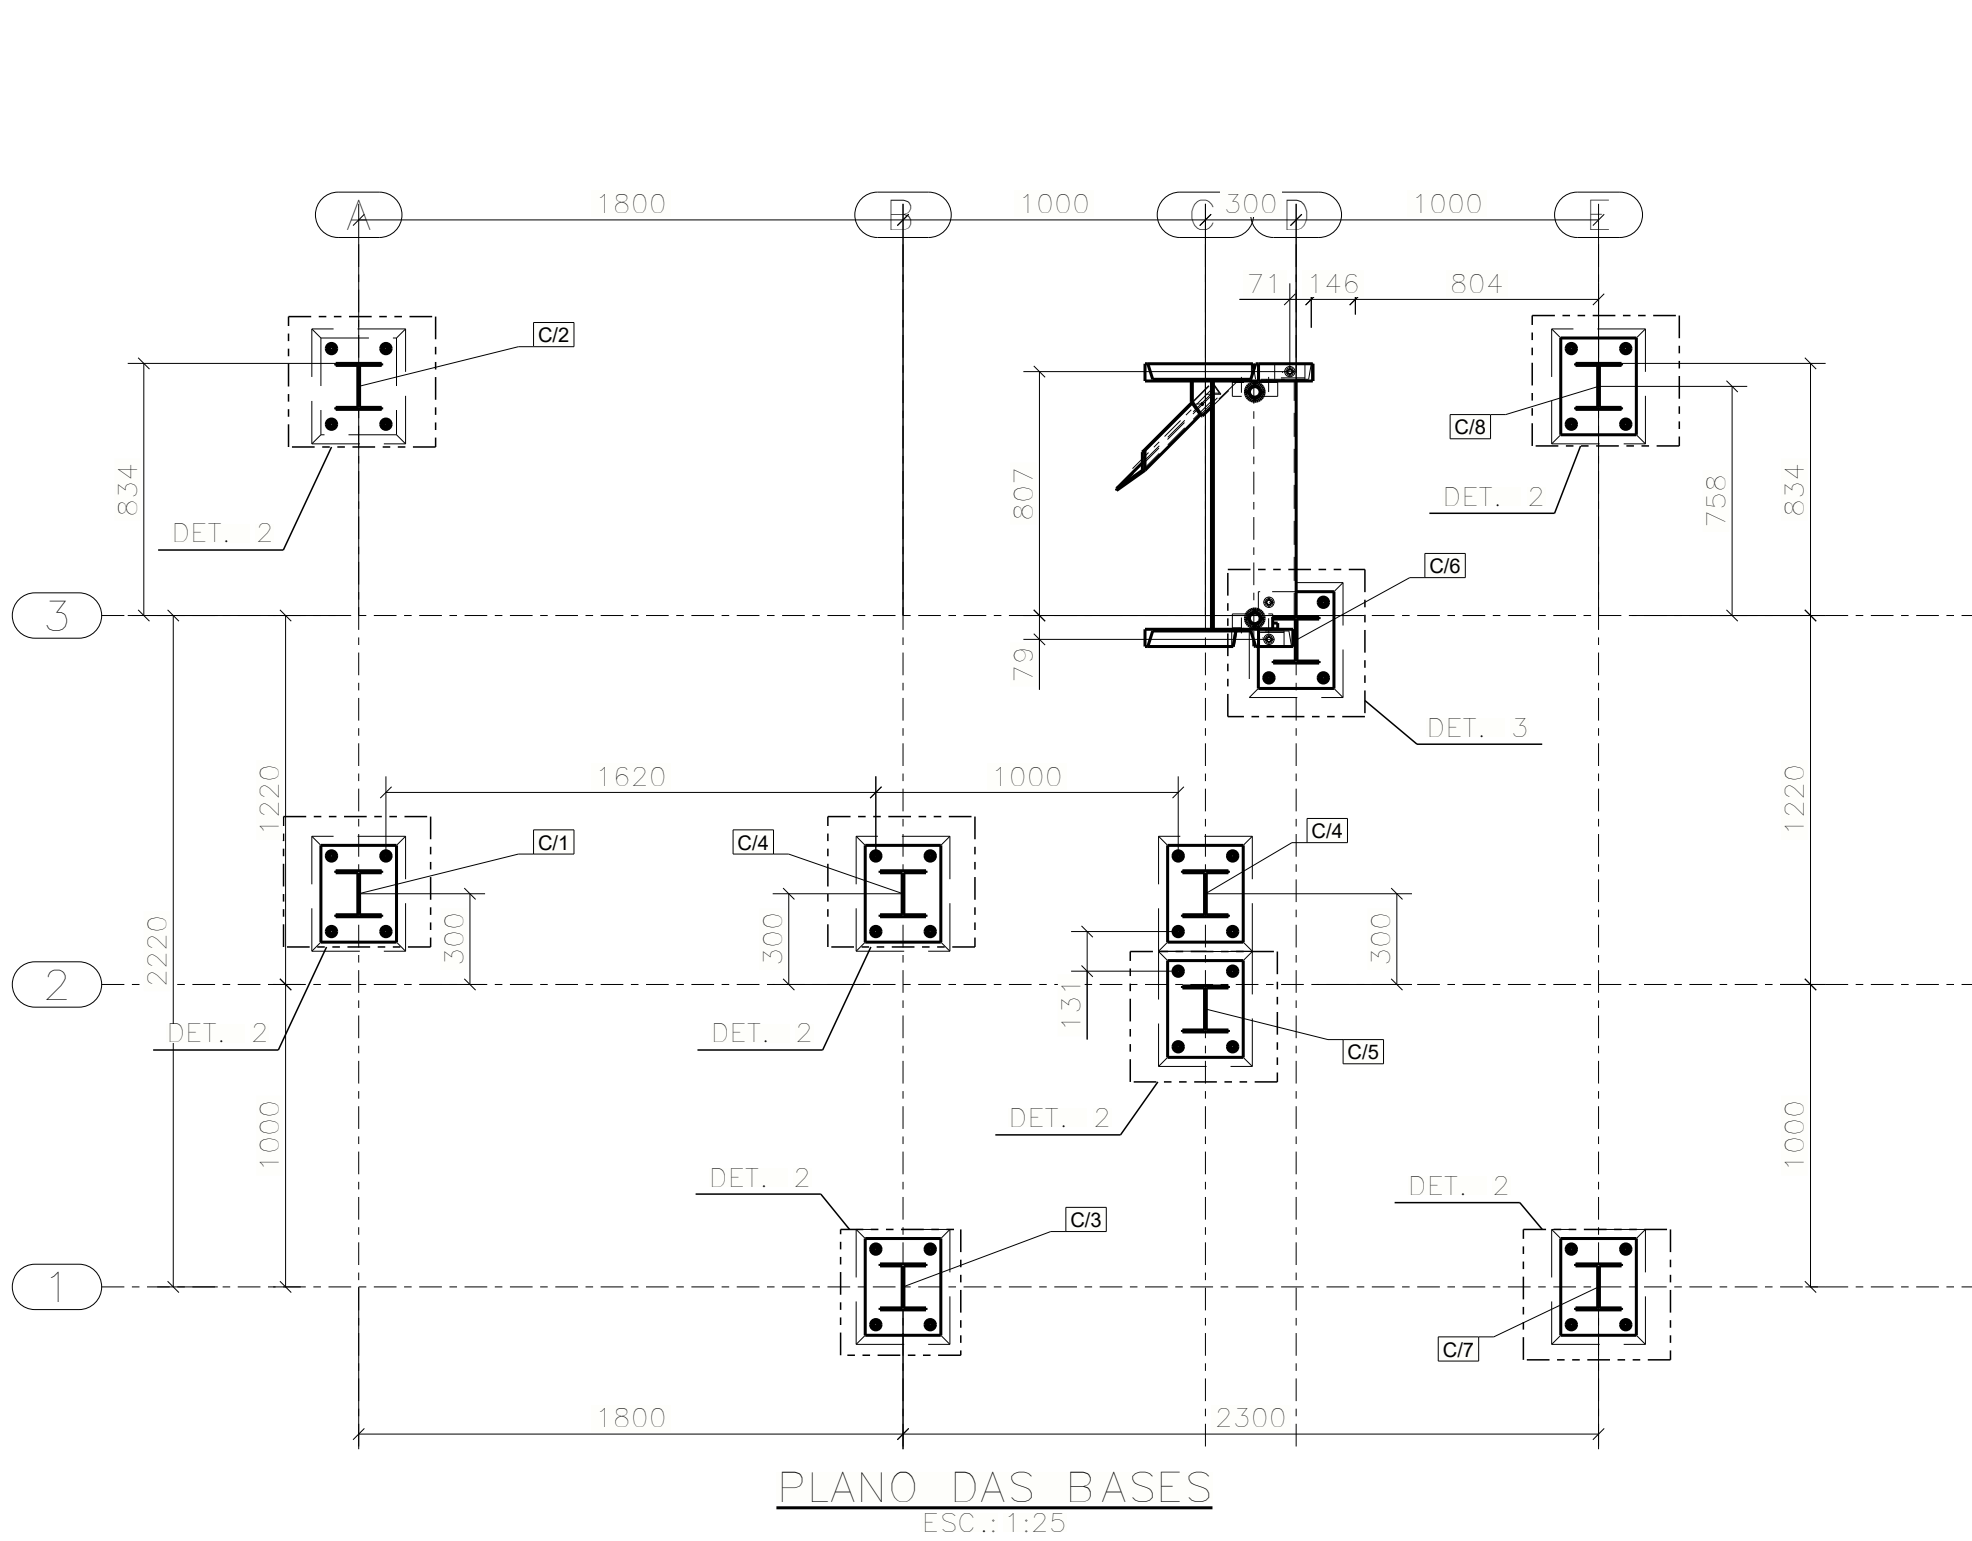

MARCA REV. (REV. MARK)		DESCRIÇÃO DA REVISÃO (DESCRIPTION)			DATA DA REVISÃO (REVISION DATE)		ORÇADO POR (CREATED BY)		VERIFICADO POR (CHECKED BY)	
Obra: CONTINENTAL - NOVO LABORATÓRIO										
Cliente: CONTINENTAL										
		Endereço:								Folha T***
		Projeto:								
		Descrição:								
		EL. DOS EIXOS 1' - 1								
RESP. TÉCNICO		Revisão								
		Escalas		Desenho		Etapa do Projeto		Formato		
		Contrato Nº		Escala de Plotar 1/1		Arquivo		A1		
		CREA-BA 051861428-0		R Engenharia Estrutural rafaelctavares@gmail.com - tel.: 71 99609-1737				841x594		